


# Mein neues Projekt

GESAMTFLÄCHE: 91.52 m<sup>2</sup> • WOHNFLÄCHE: 14.96 m<sup>2</sup> • ETAGEN: 1 • RÄUME: 2

**m** magicplan

## ▼ DEMO Tannenweg 3a

GESAMTFLÄCHE: 91.52 m<sup>2</sup> • WOHNFLÄCHE: 14.96 m<sup>2</sup> • RÄUME: 2

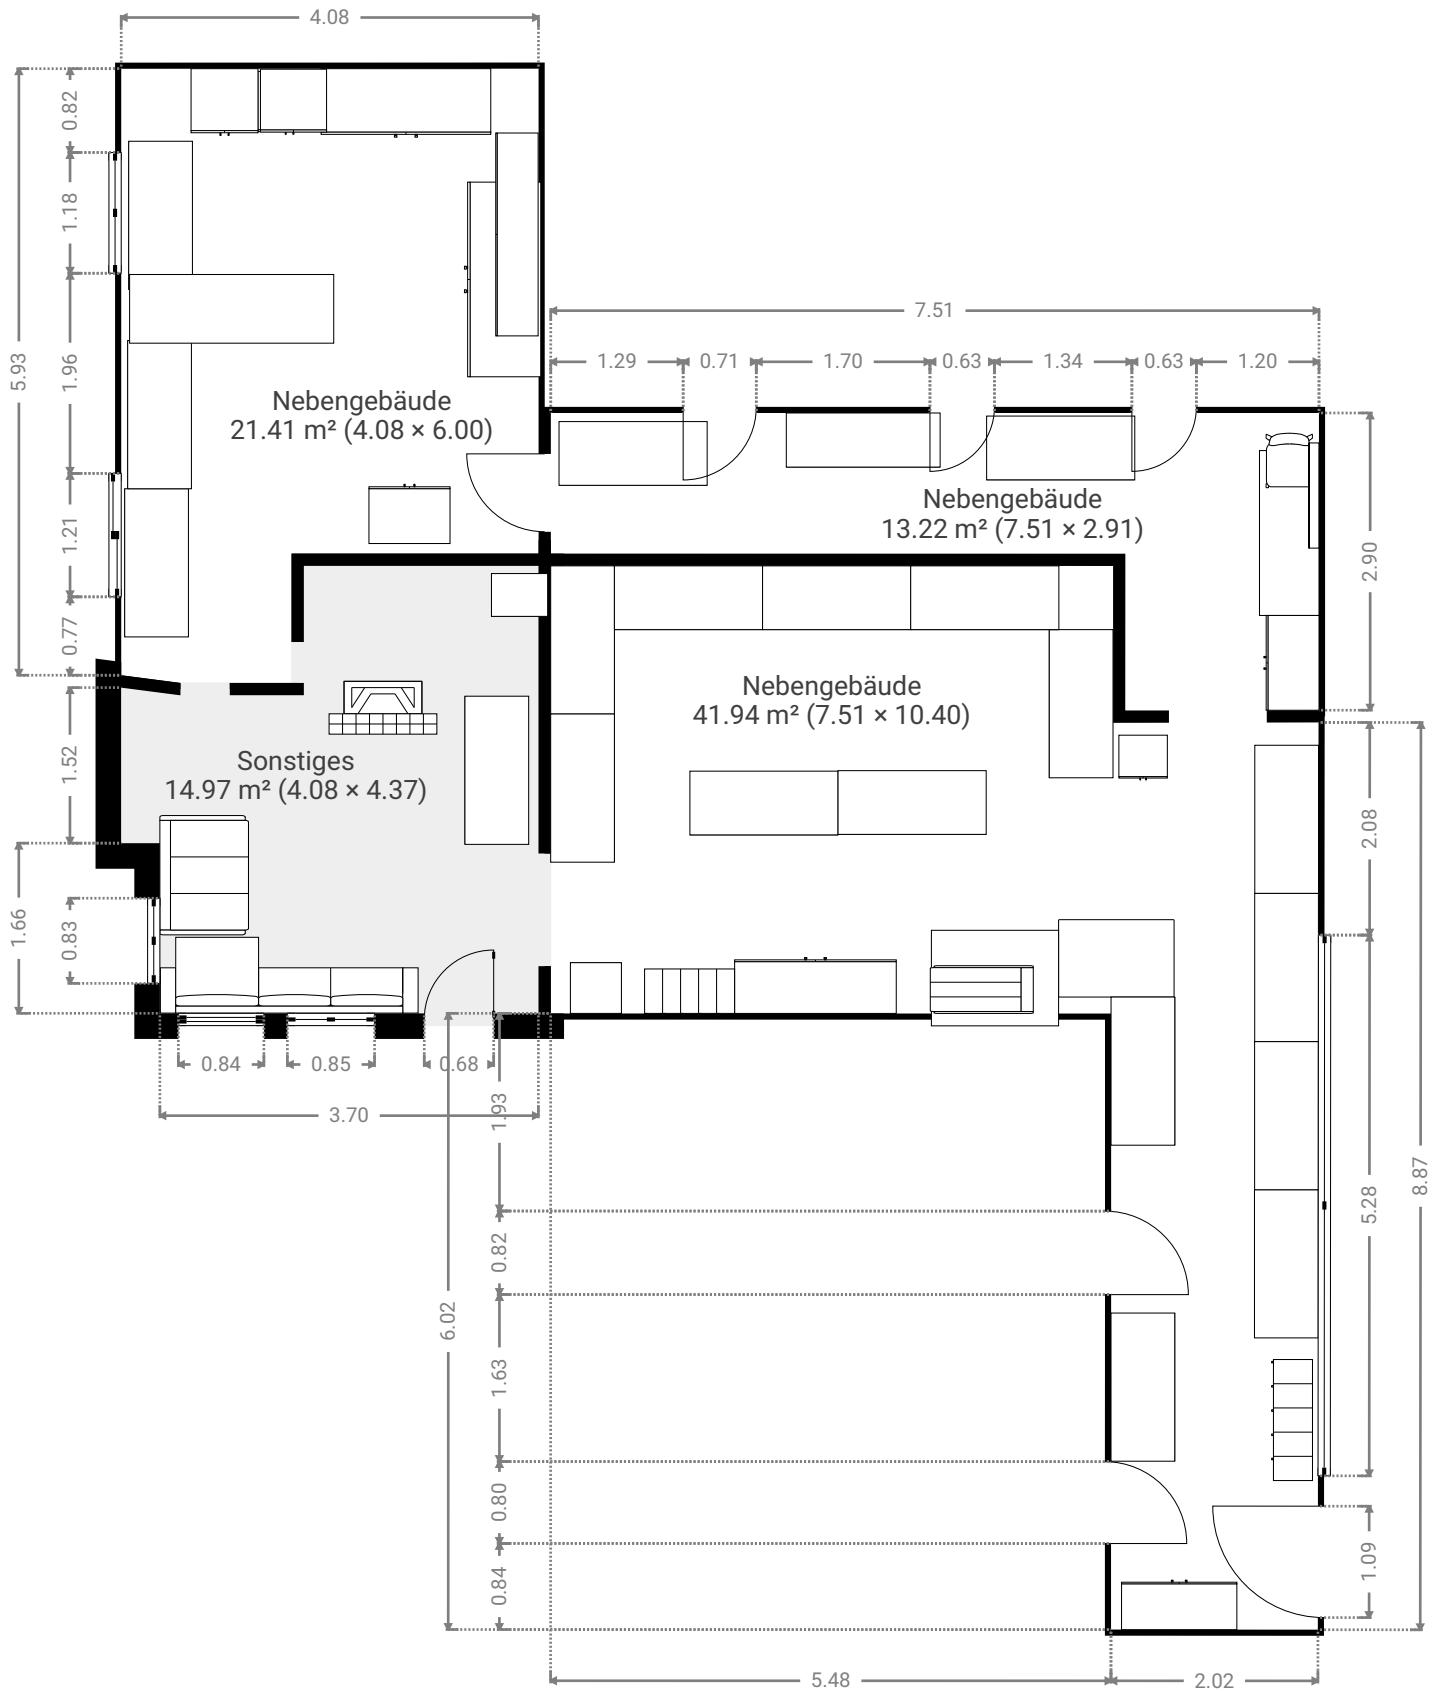

DIESER GRUNDRISS WIRD OHNE JEGLICHE GEWÄHRLEISTUNG ZUR VERFÜGUNG GESTELLT. SENSOPIA LEHNT JEDE GARANTIE AB, EINSCHLIESSLICH, OHNE EINSCHRÄNKUNG, ZUFRIEDENSTELLENDER QUALITÄT ODER GENAUIGKEIT DER ABMESSUNGEN.

0 1 2 3m  
1:74  
Page 1/1